

PRELIMINARY
NOT FOR CONSTRUCTION

tillmann
architects ruth
robinson

STAMP

STAMP


THE INFORMATION CONTAINED ON THIS DRAWING WAS PREPARED BY
architects TILLMANN RUTH ROBINSON inc. AND IS PROTECTED BY
COPYRIGHT. REPRODUCTION BY ANY MEANS OF THE INFORMATION
CONTAINED ON THIS DRAWING, IN WHOLE OR IN PART IS EXPRESSLY
FORBIDDEN WITHOUT THE WRITTEN PERMISSION OF architects
TILLMANN RUTH ROBINSON inc.

No.	ISSUED FOR	DATE

DRAWING TITLE:
**LEVEL 1 PROPOSED
& DEMO FLOOR
PLAN**


DRAWN:	SCALE:	PROJECT NO:
MEB	3/16" = 1'-0"	P1368 (atRR)
CHECKED:	DATE:	
SWR	JULY 20, 2023	

A-201

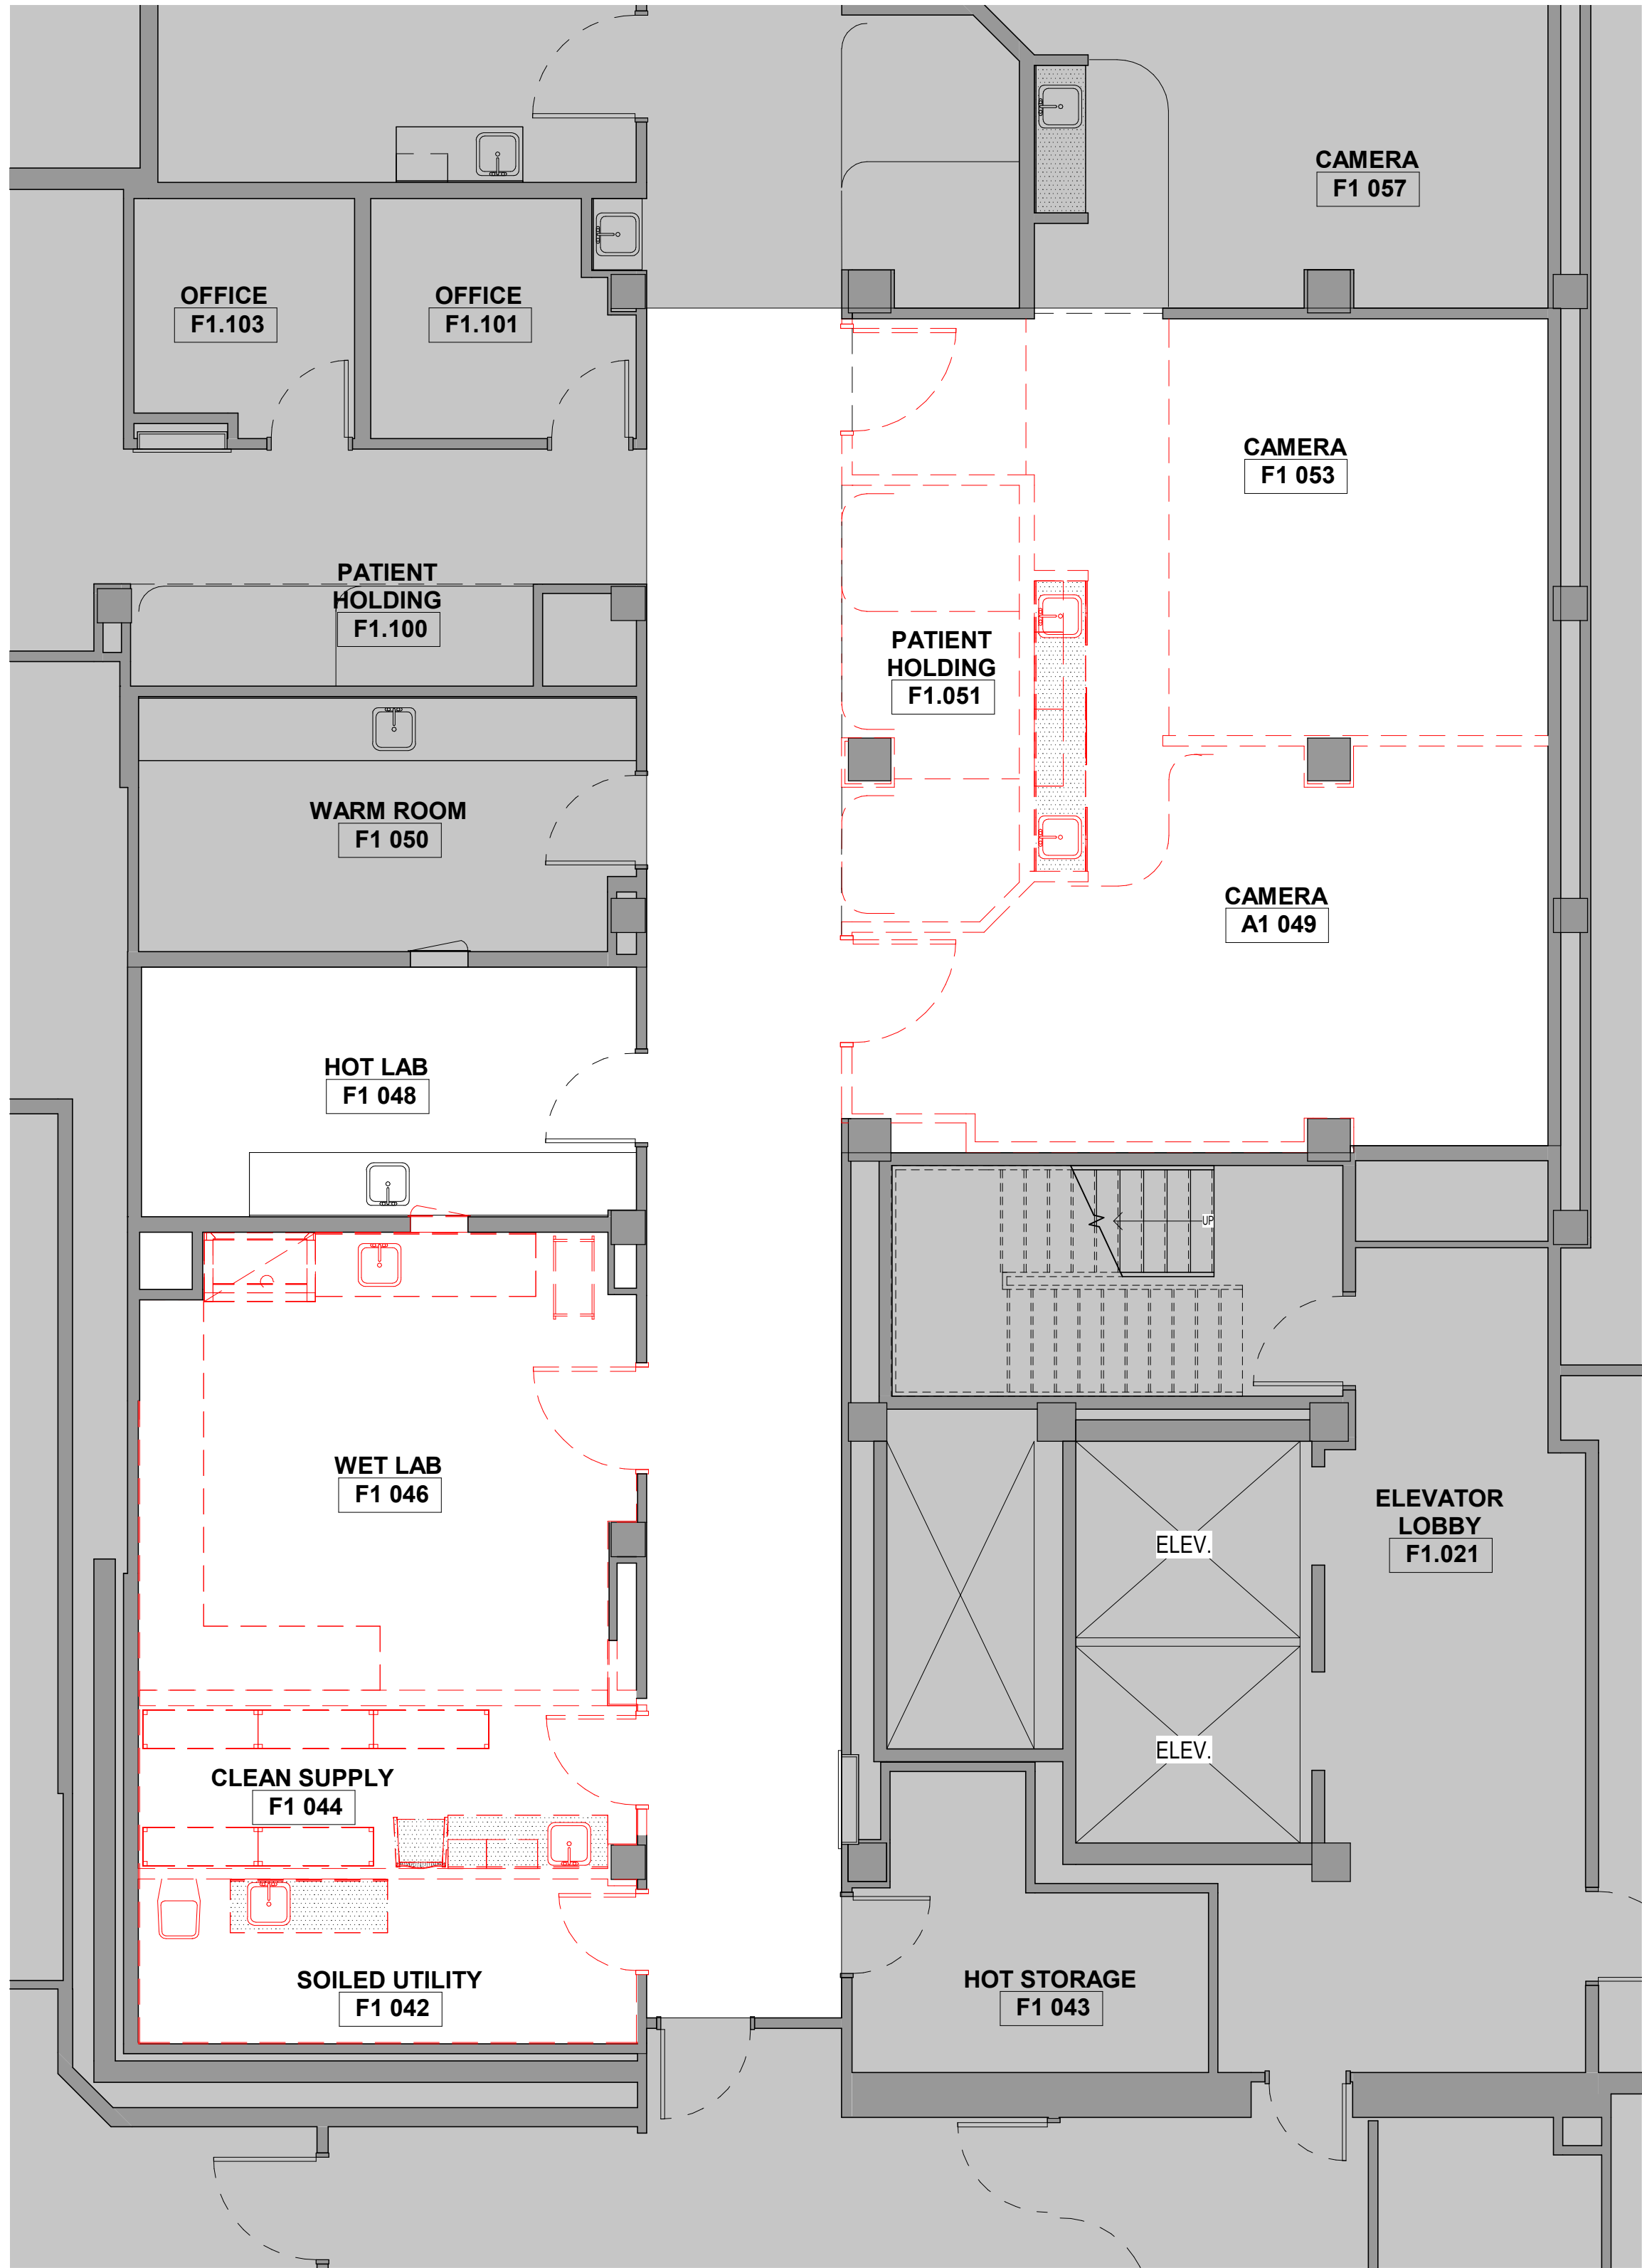

LEVEL 1 DEMOLITION FLOOR PLAN

3/16" = 1'-0"

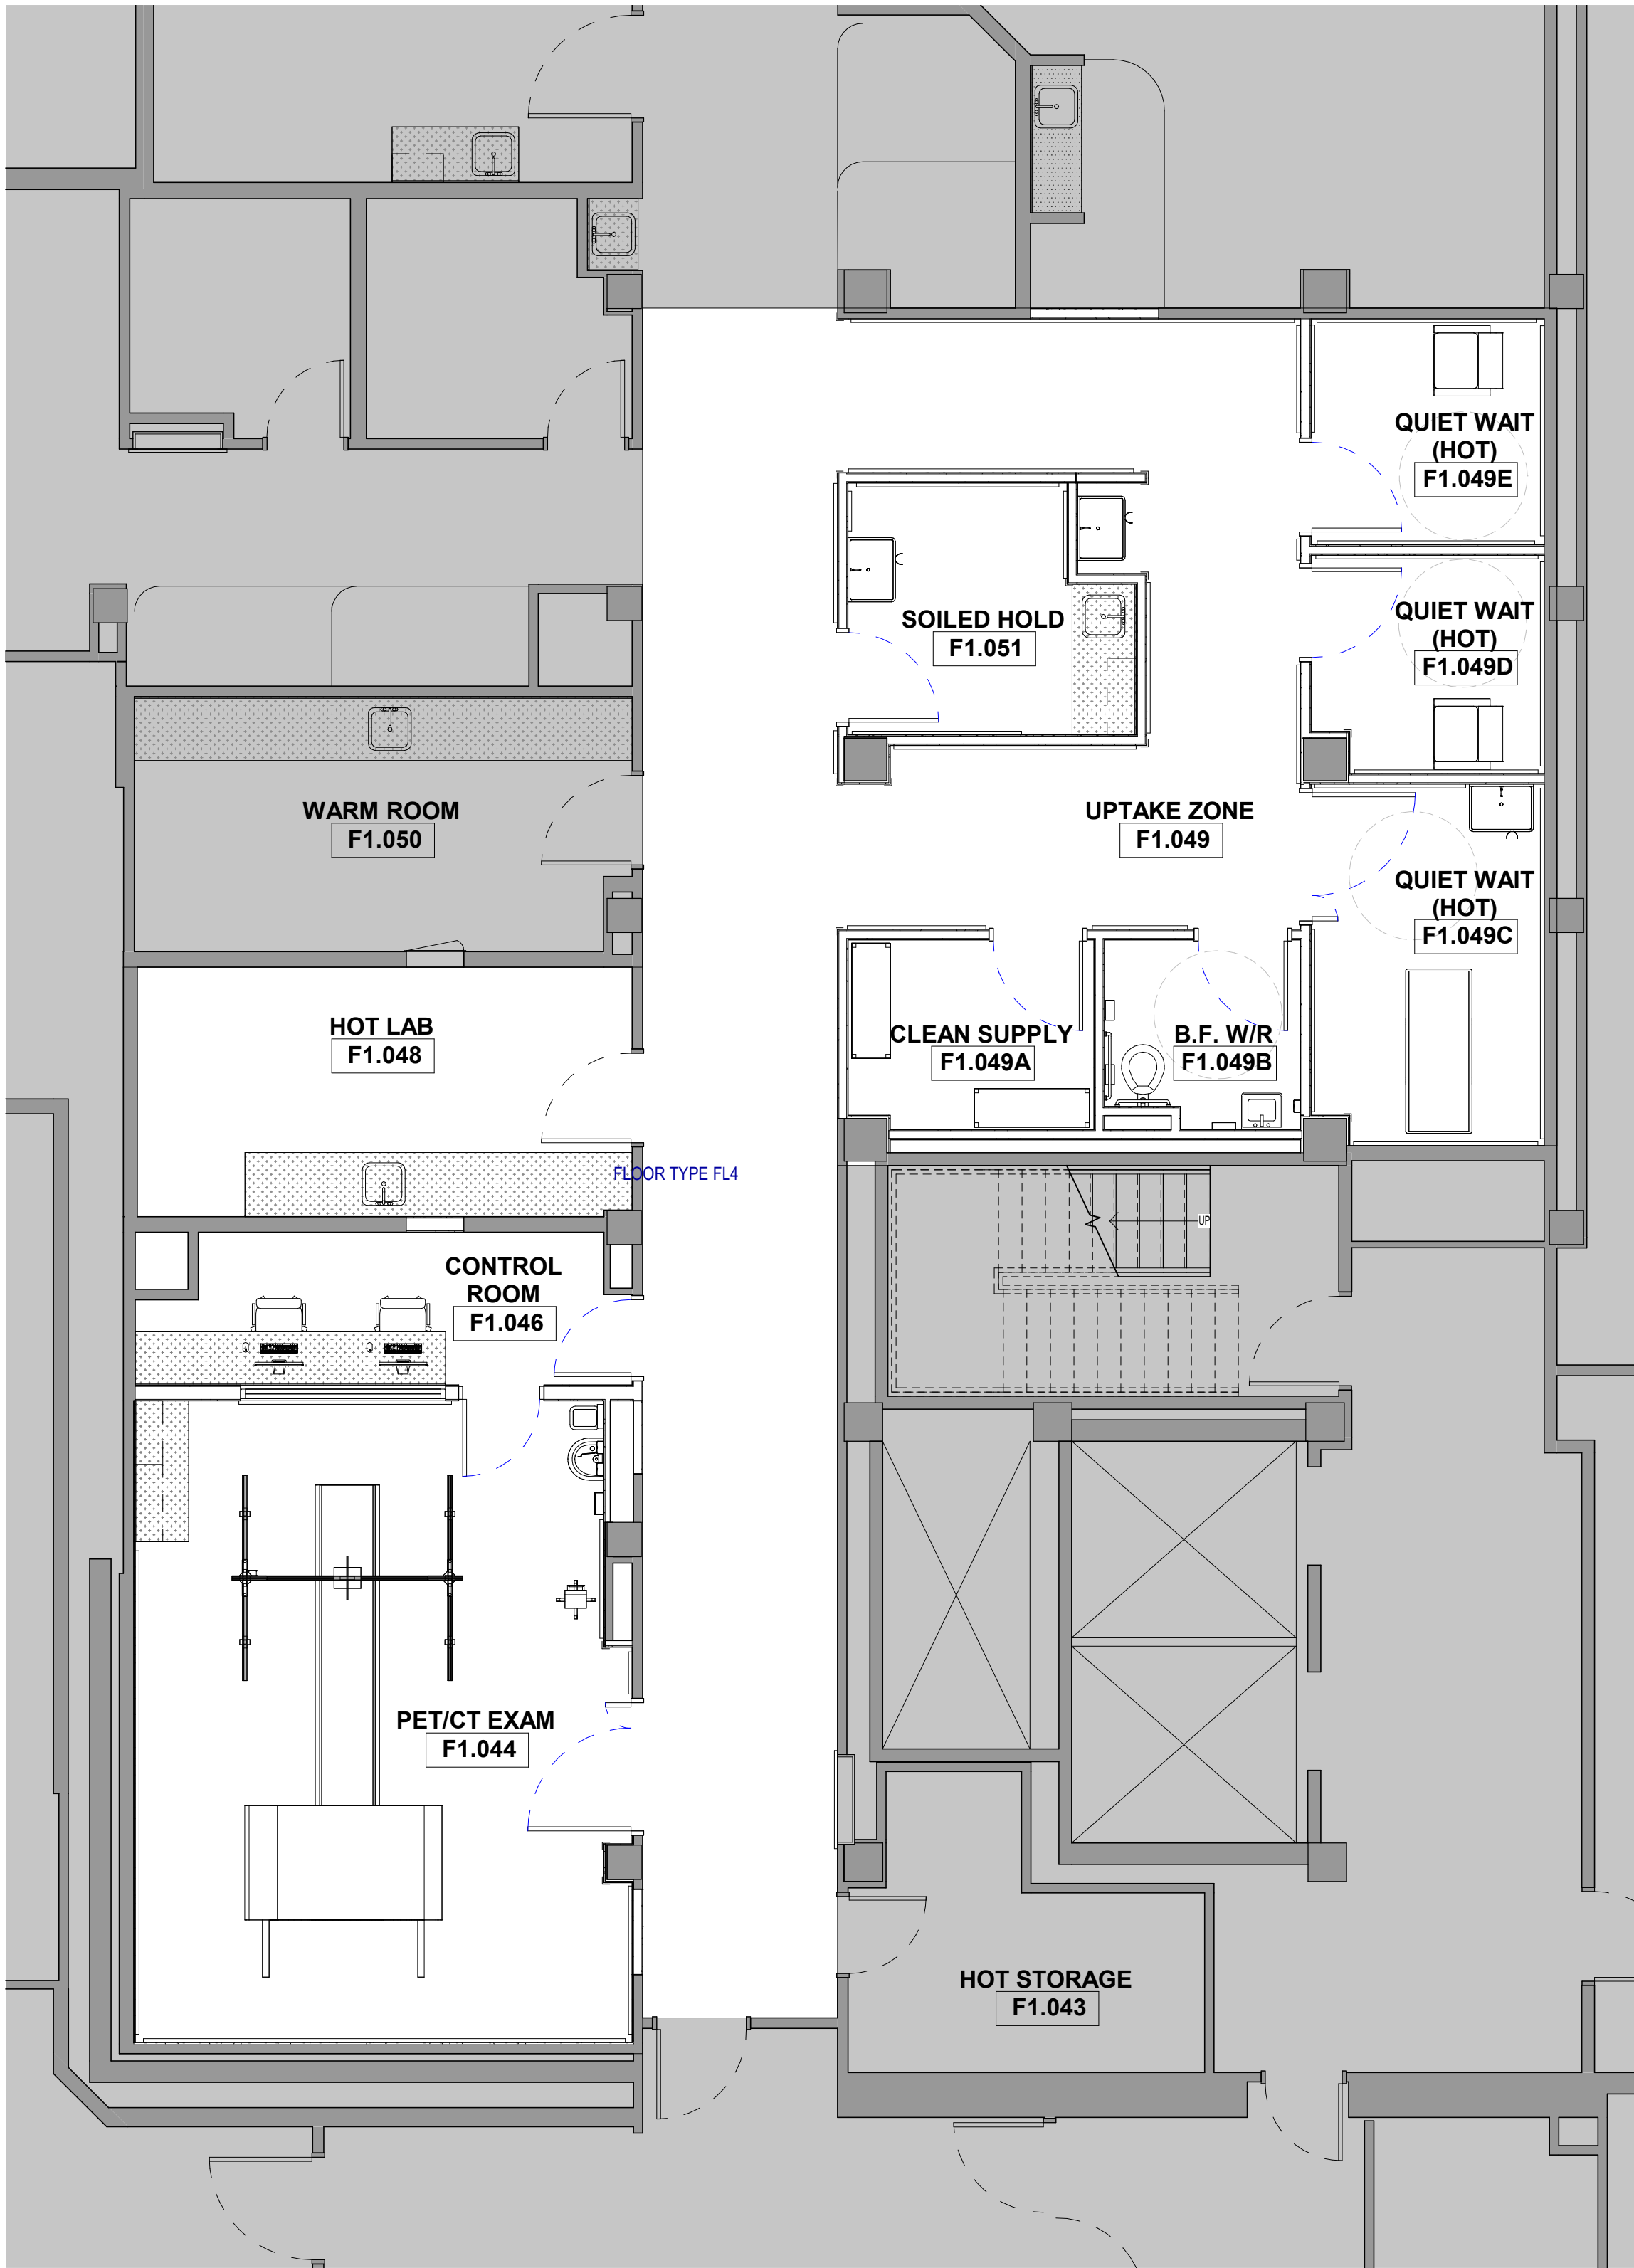

PROPOSED LEVEL 1 FLOOR PLAN

3/16" = 1'-0"

C:\Users\meel\Documents\P1368 - Lakeridge PET_CT Scanner\P1368 - Lakeridge PET_CT Scanner (Local 2022) MEB.dwg 7/20/2023 8:59:56 AM